


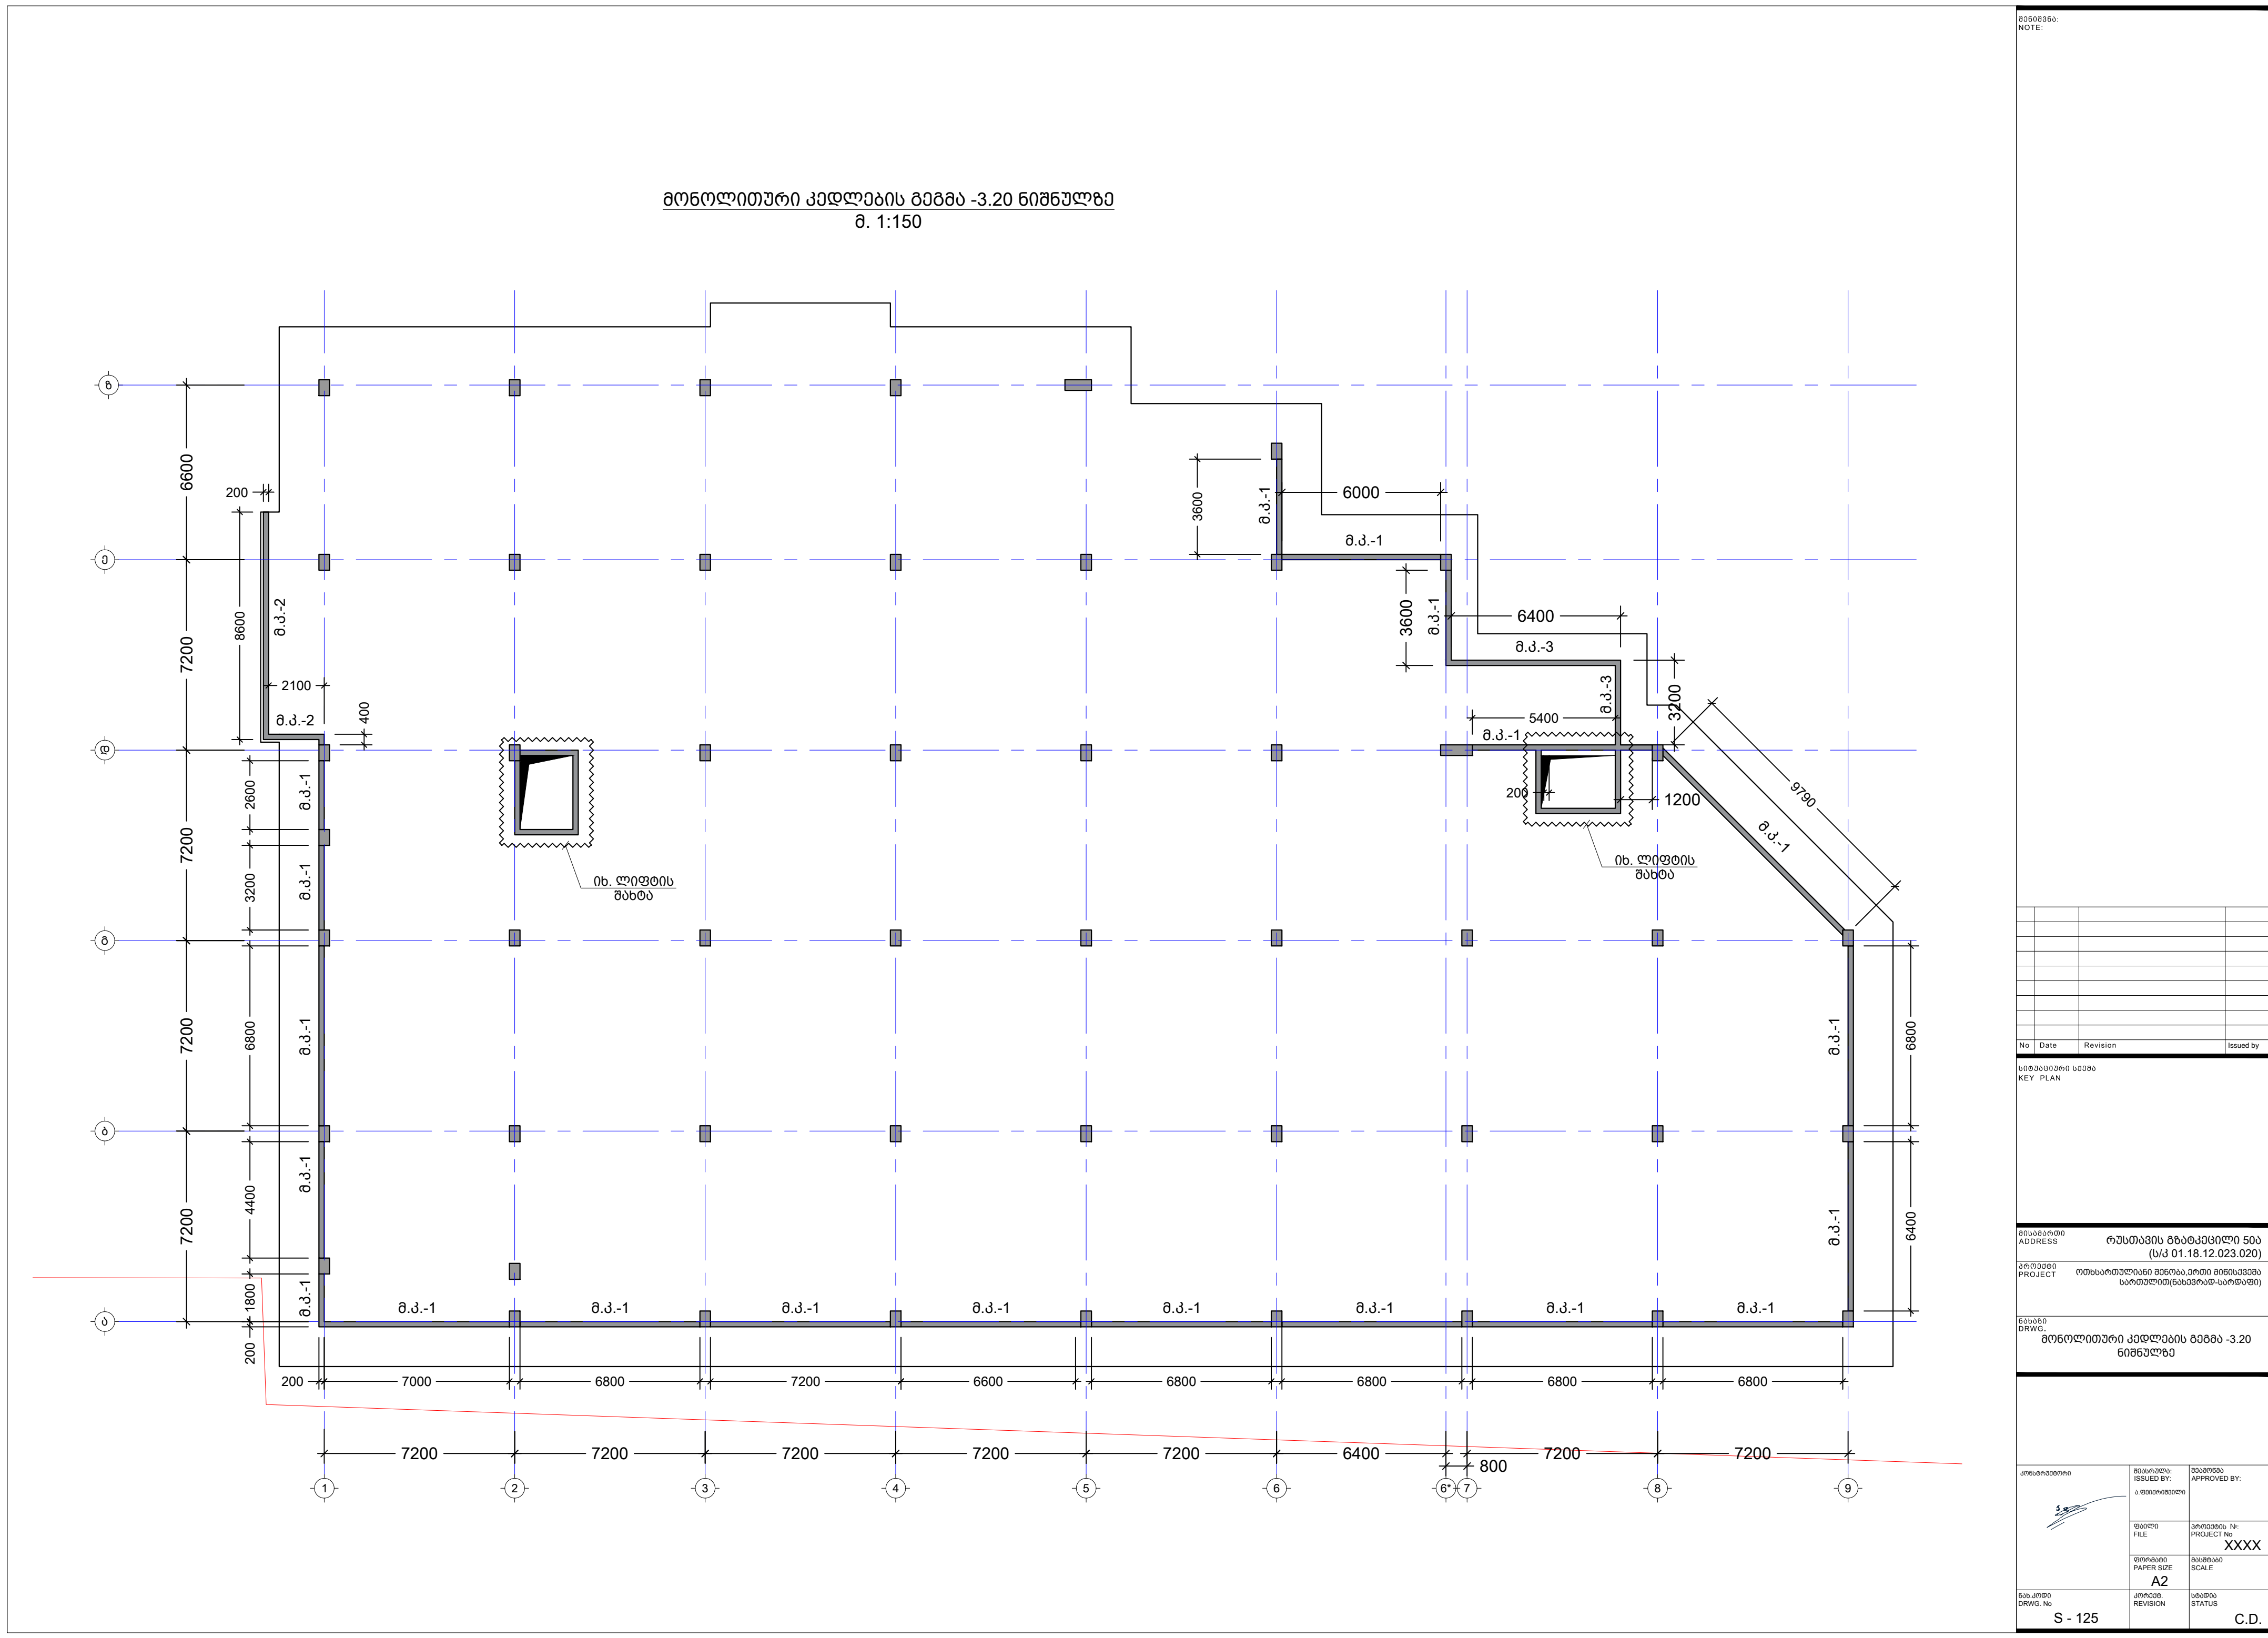

მონოლითური კედლების გეგმა -3.20 ნიშნულზე მ. 1:150	
Architectural key plan showing building layout with dimensions and labels.	
<table><tr><td>No</td><td>Date</td><td>Revision</td><td>Issued by</td></tr><tr><td> </td><td> </td><td> </td><td> </td></tr><tr><td> </td><td> </td><td> </td><td> </td></tr><tr><td> </td><td> </td><td> </td><td> </td></tr><tr><td> </td><td> </td><td> </td><td> </td></tr><tr><td> </td><td> </td><td> </td><td> </td></tr><tr><td> </td><td> </td><td> </td><td> </td></tr><tr><td> </td><td> </td><td> </td><td> </td></tr><tr><td> </td><td> </td><td> </td><td> </td></tr><tr><td> </td><td> </td><td> </td><td> </td></tr></table>				No	Date	Revision	Issued by																																				
No	Date	Revision	Issued by	
სტრუქტურული სკეტი KEY PLAN	
<table><tr><td>მისამართი ADDRESS</td><td>რუსთავეის მუნიციპალიტეტი 50ა (ს/პ 01.18.12.023.020)</td></tr><tr><td>პროექტი PROJECT</td><td>ოთხსართულიანი მონოლითური მიწისკვეთის სართული(ნახევრად-სართული)</td></tr></table>				მისამართი ADDRESS	რუსთავეის მუნიციპალიტეტი 50ა (ს/პ 01.18.12.023.020)	პროექტი PROJECT	ოთხსართულიანი მონოლითური მიწისკვეთის სართული(ნახევრად-სართული)																																				
მისამართი ADDRESS	რუსთავეის მუნიციპალიტეტი 50ა (ს/პ 01.18.12.023.020)	
პროექტი PROJECT	ოთხსართულიანი მონოლითური მიწისკვეთის სართული(ნახევრად-სართული)	
ნახაზი DRWG. მონოლითური კედლების გეგმა -3.20 ნიშნულზე	
<table><tr><td>კონსტრუქტორი</td><td>მასშტაბი: ISSUED BY: ა. მამუკაშვილი</td><td>შეამოწმა: APPROVED BY:</td></tr><tr><td></td><td>ფაილი FILE</td><td>პროექტის №: PROJECT No XXXX</td></tr><tr><td></td><td>ფორმატი PAPER SIZE A2</td><td>მასშტაბი SCALE</td></tr><tr><td>ნახ. კომპი DRWG. No S - 125</td><td>კომპი REVISION</td><td>სტატუსი STATUS C.D.</td></tr></table>				კონსტრუქტორი	მასშტაბი: ISSUED BY: ა. მამუკაშვილი	შეამოწმა: APPROVED BY:		ფაილი FILE	პროექტის №: PROJECT No XXXX		ფორმატი PAPER SIZE A2	მასშტაბი SCALE	ნახ. კომპი DRWG. No S - 125	კომპი REVISION	სტატუსი STATUS C.D.																												
კონსტრუქტორი	მასშტაბი: ISSUED BY: ა. მამუკაშვილი	შეამოწმა: APPROVED BY:	
	ფაილი FILE	პროექტის №: PROJECT No XXXX	
	ფორმატი PAPER SIZE A2	მასშტაბი SCALE	
ნახ. კომპი DRWG. No S - 125	კომპი REVISION	სტატუსი STATUS C.D.	